
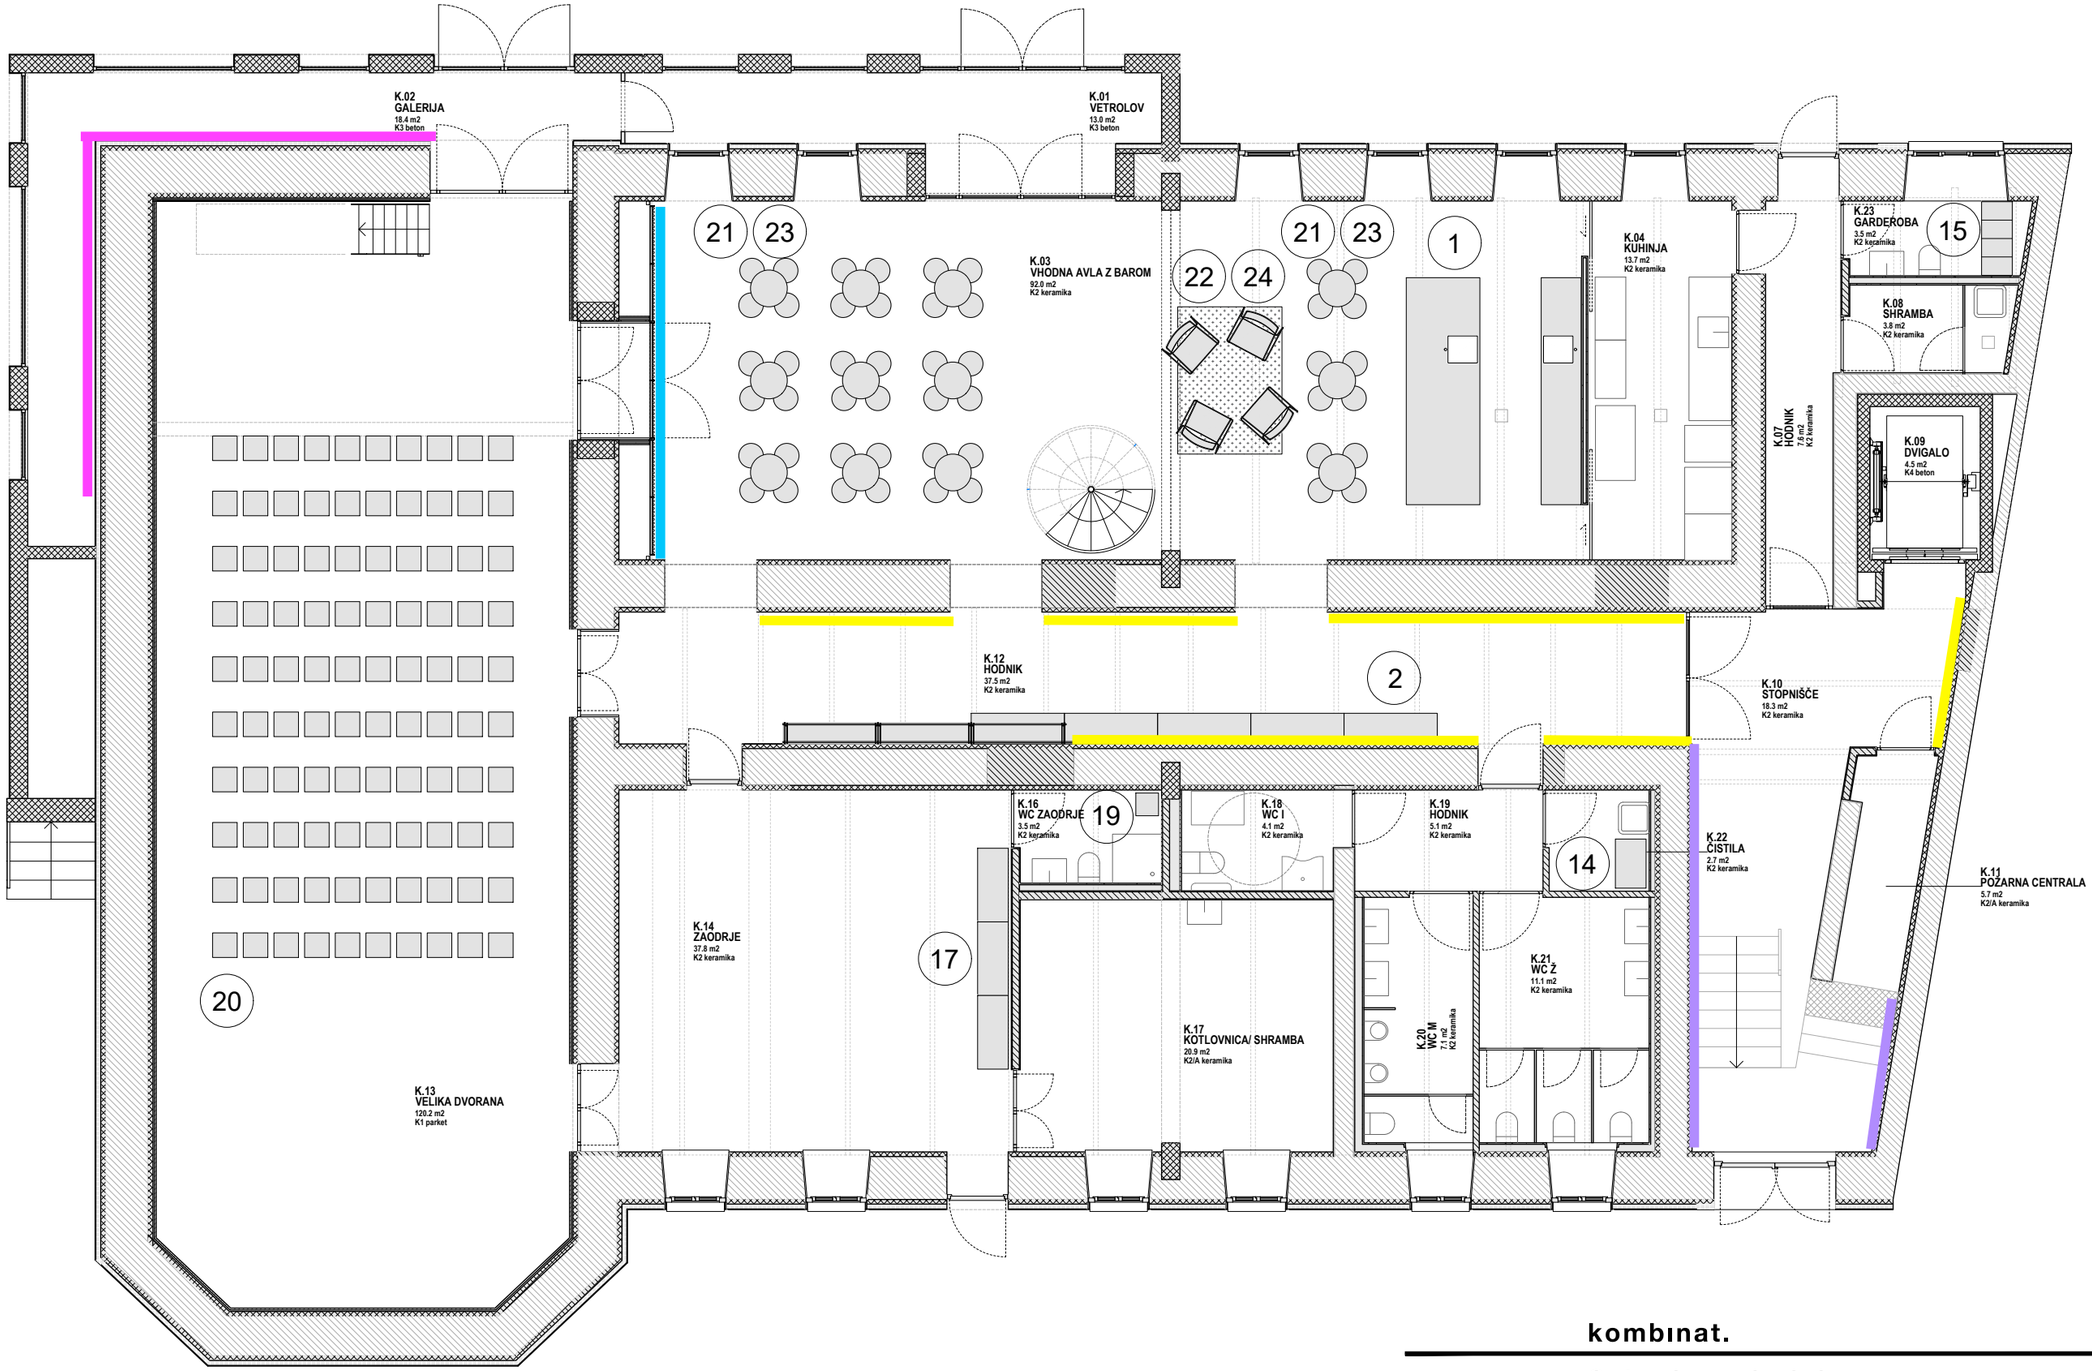


kombinat.

objekt	**Center urbanega dogajanja**		
številka načrta	360/23	datum	november 2024
merilo	1:100	sprememba	/

01 POZICIJSKI NAČRT OPREME_KLET

© kombinat d.o.o. uporaba dela projekta ali celote samo s pisnim soglasjem avtorjev

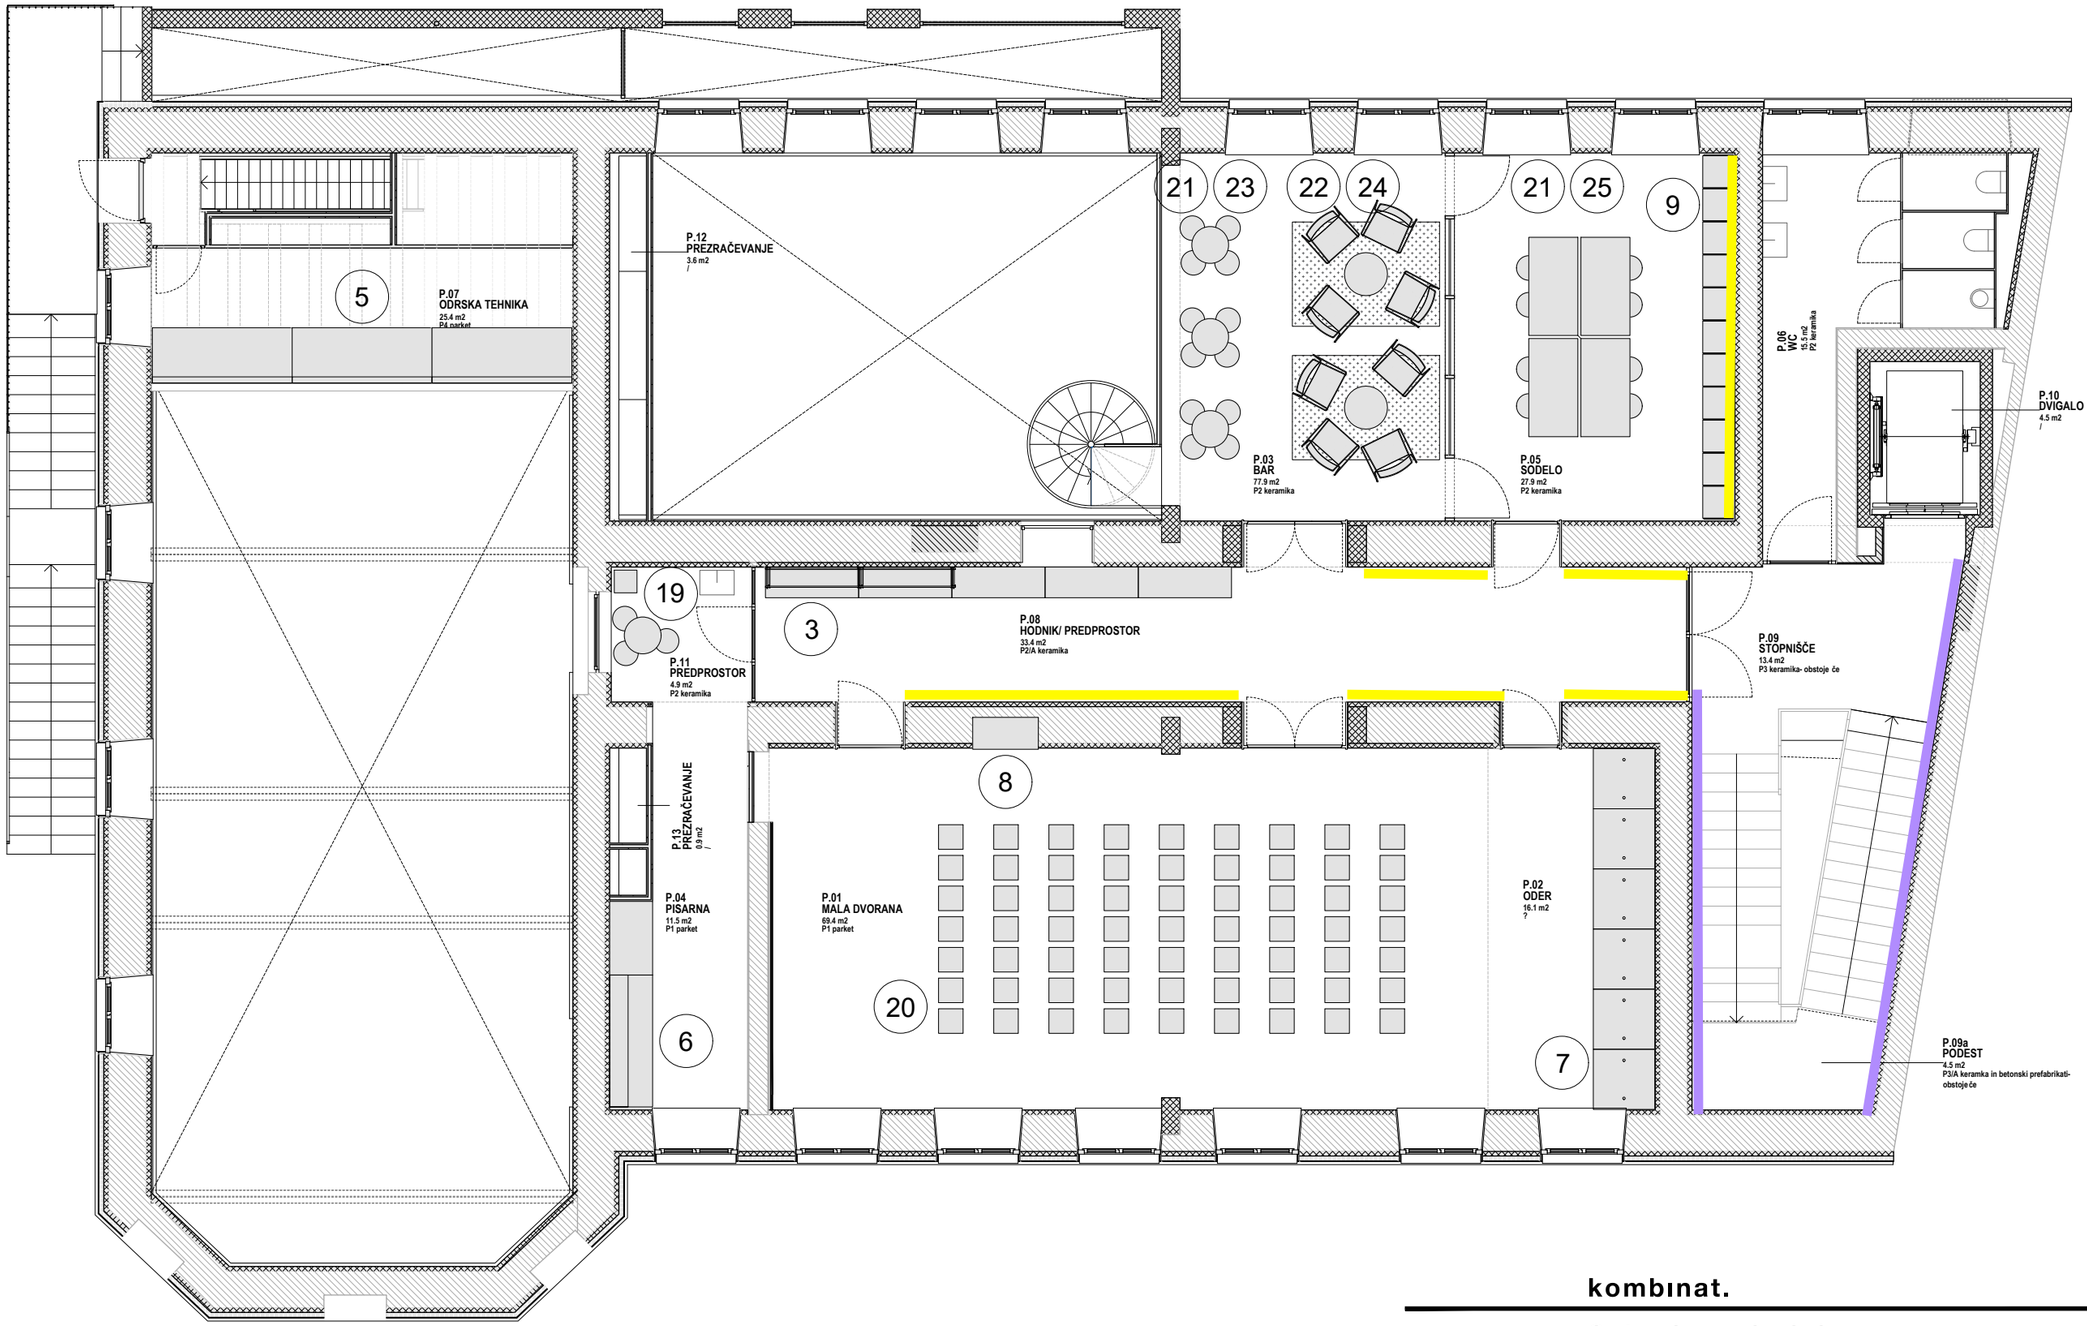


kombinat.

objekt	**Center urbanega dogajanja**		
številka načrta	360/23	datum	november 2024
merilo	1:100	sprememba	/

02 POZICIJSKI NAČRT OPREME_PRITLIČJE

© kombinat d.o.o. uporaba dela projekta ali celote samo s pisnim soglasjem avtorjev

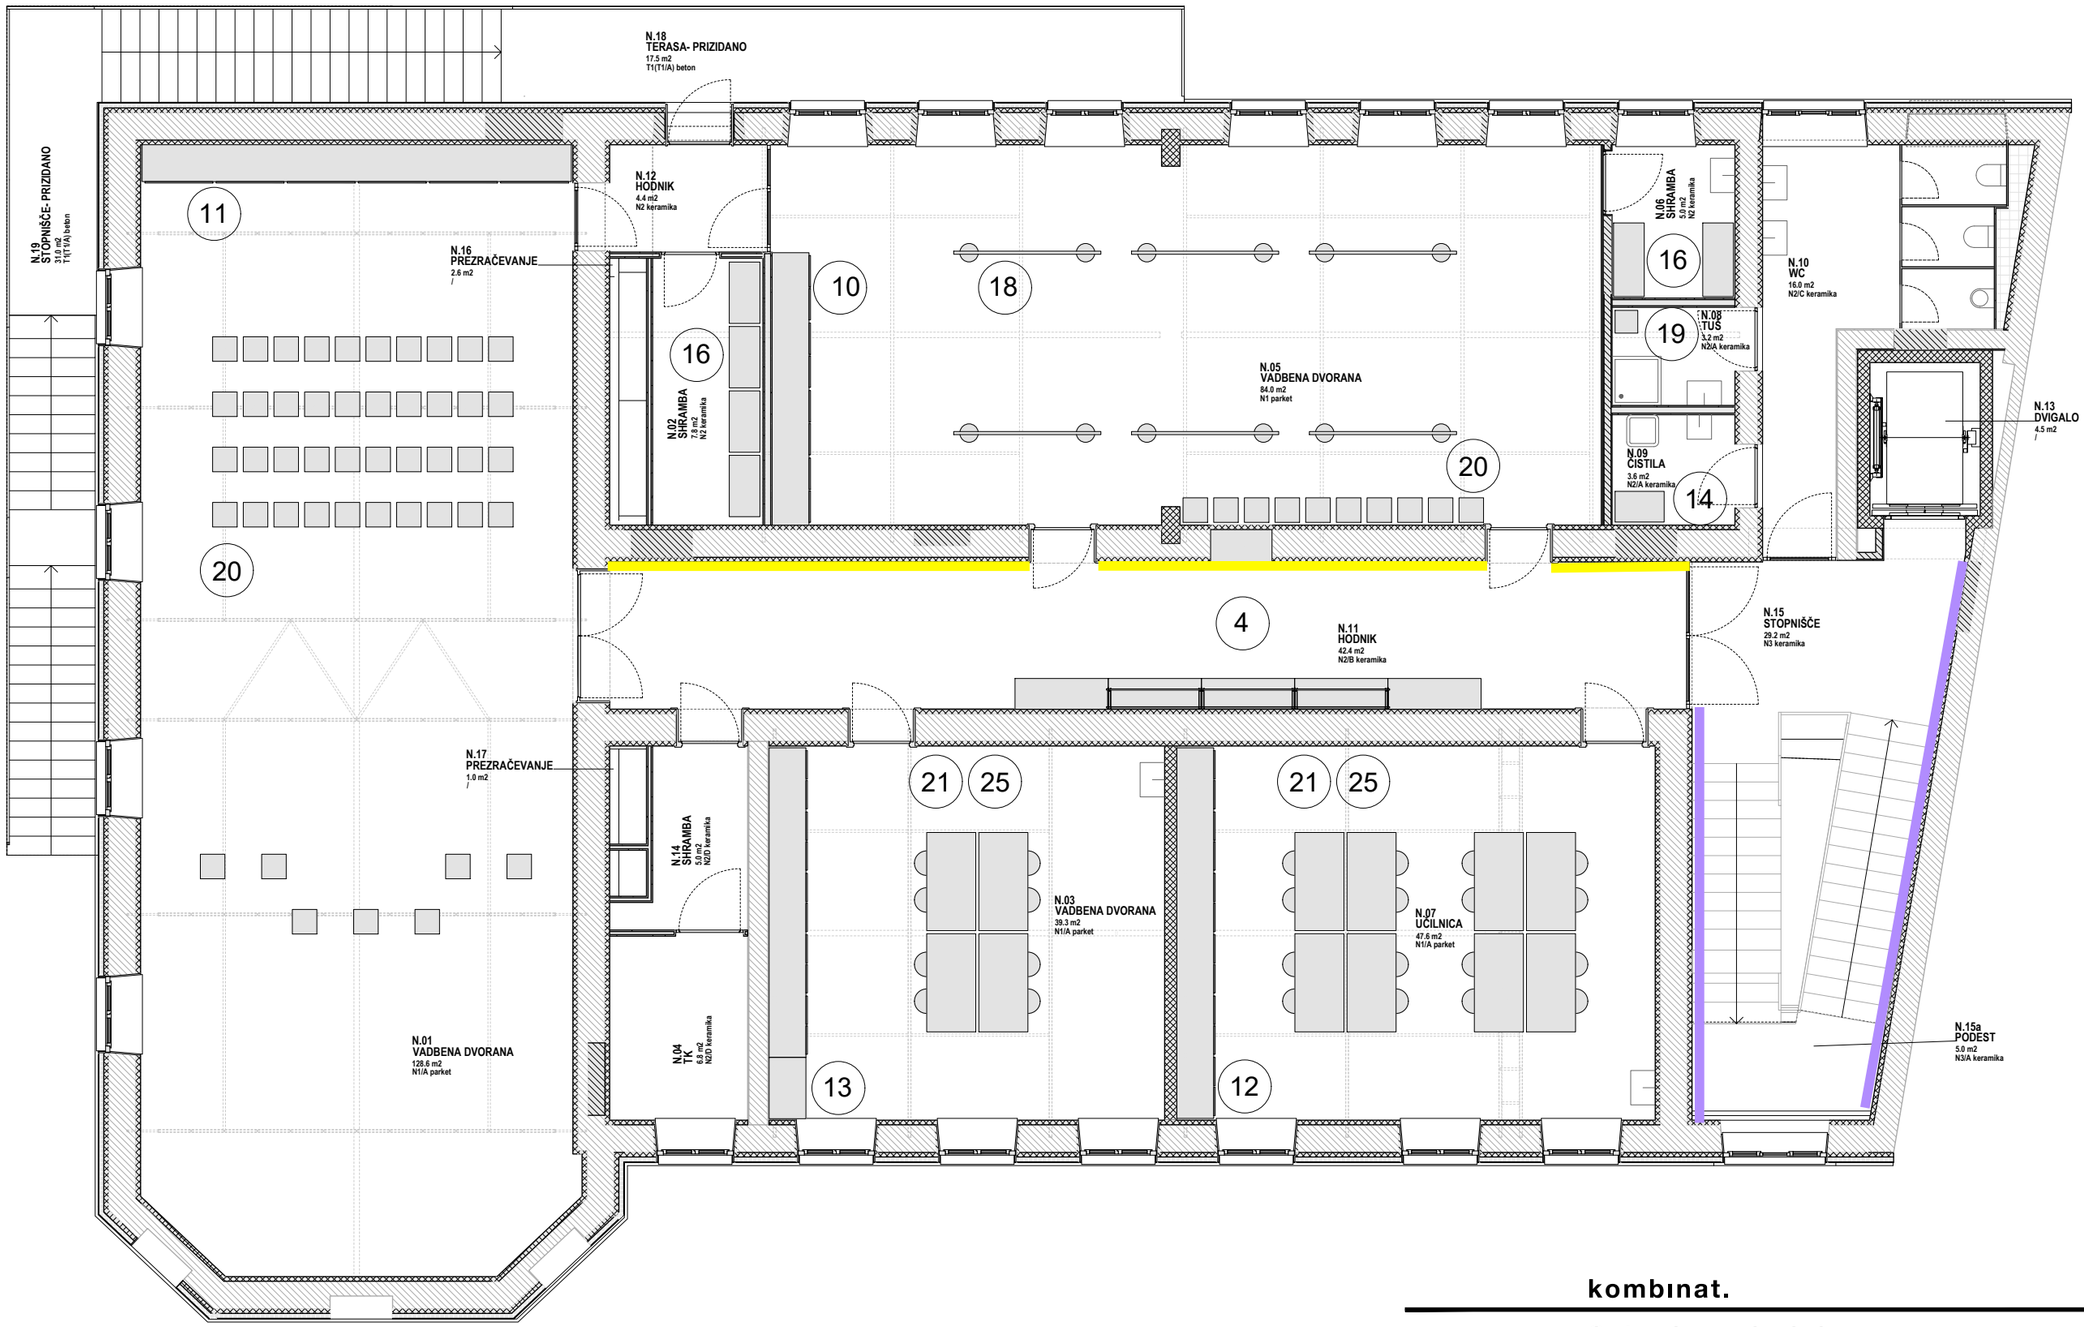

kombinat.

objekt	**Center urbanega dogajanja**		
številka načrta	360/23	datum	november 2024
merilo	1:100	sprememba	/

03 POZICIJSKI NAČRT OPREME_1.NADSTROPJE

© kombinat d.o.o. uporaba dela projekta ali celote samo s pisnim soglasjem avtorjev